


DẦM DX3 - TẦNG 1 (4 NHỊP • B 200X400) - L = 21.85m

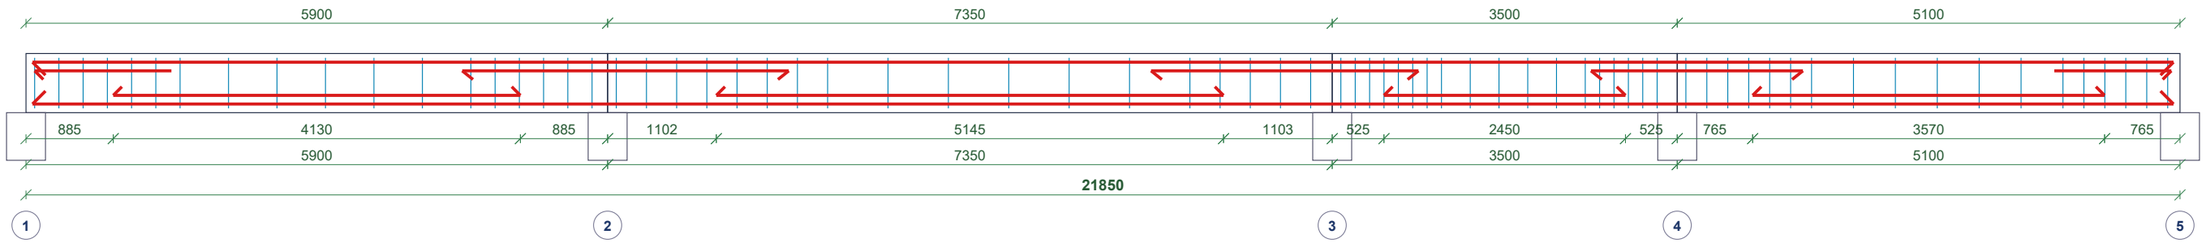

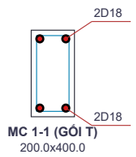

MC 1-1 (GỐI T)
200.0x400.0

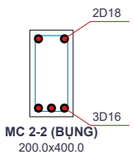

MC 2-2 (BỤNG)
200.0x400.0



MC 3-3 (GỐI P)
200.0x400.0