
MẶT BẰNG KÝ HIỆU DẦM SÀN TẦNG 3 • CAO ĐỘ +11.800

DỰ ÁN: CẢI TẠO PHƯƠNG ÁN B • TIÊU CHUẨN: TCVN 5574:2018 • BỐ TRÍ DẦM THEO ĐÚNG BỀ RỘNG VÀ KÝ HIỆU (DX / DY)

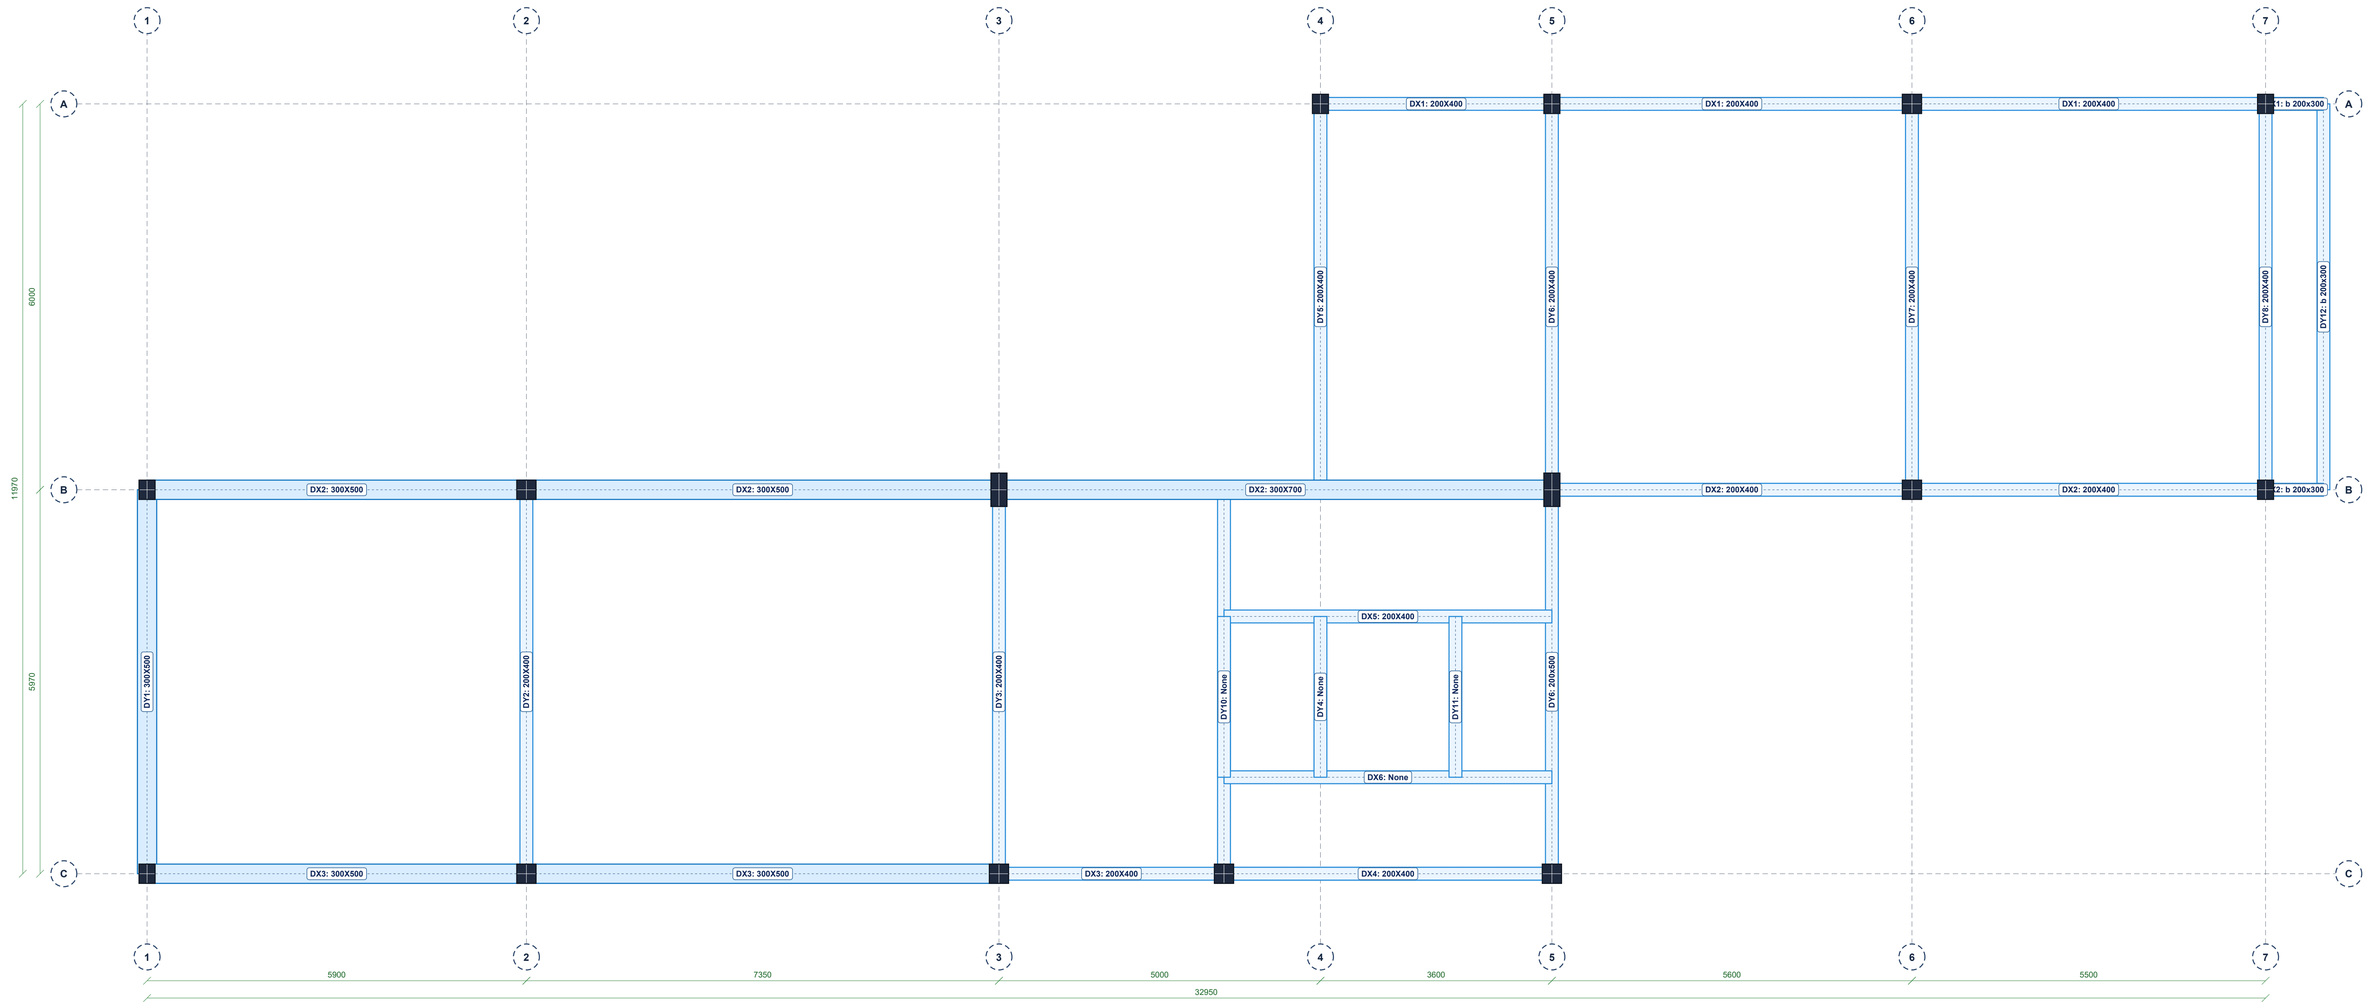

CHÚ DẪN MẶT BẰNG KÝ HIỆU DẦM KẾT CẤU (TCVN 5574:2018):

1. Ký hiệu dầm: DX (Dầm phương X chạy dọc nhà) • DY (Dầm phương Y chạy ngang nhà).
2. Tất cả thép đai dầm và cột quy chuẩn về Φ6 (d6a100/200). Bê tông dầm sàn B22.5 (M300).