
MẶT BẰNG ĐỊNH VỊ VÀ BỐ TRÍ CỘT (TOÀN NHÀ - ĐÚNG INDEX C1 → C18)

HỆ LƯỚI TRỤC 1-7 (32.95m) × TRỤC A-C (11.97m) • 15 VỊ TRÍ CỘT CHÍNH • ĐÚNG KÍCH THƯỚC TIẾT DIỆN & TIM ĐỊNH VỊ

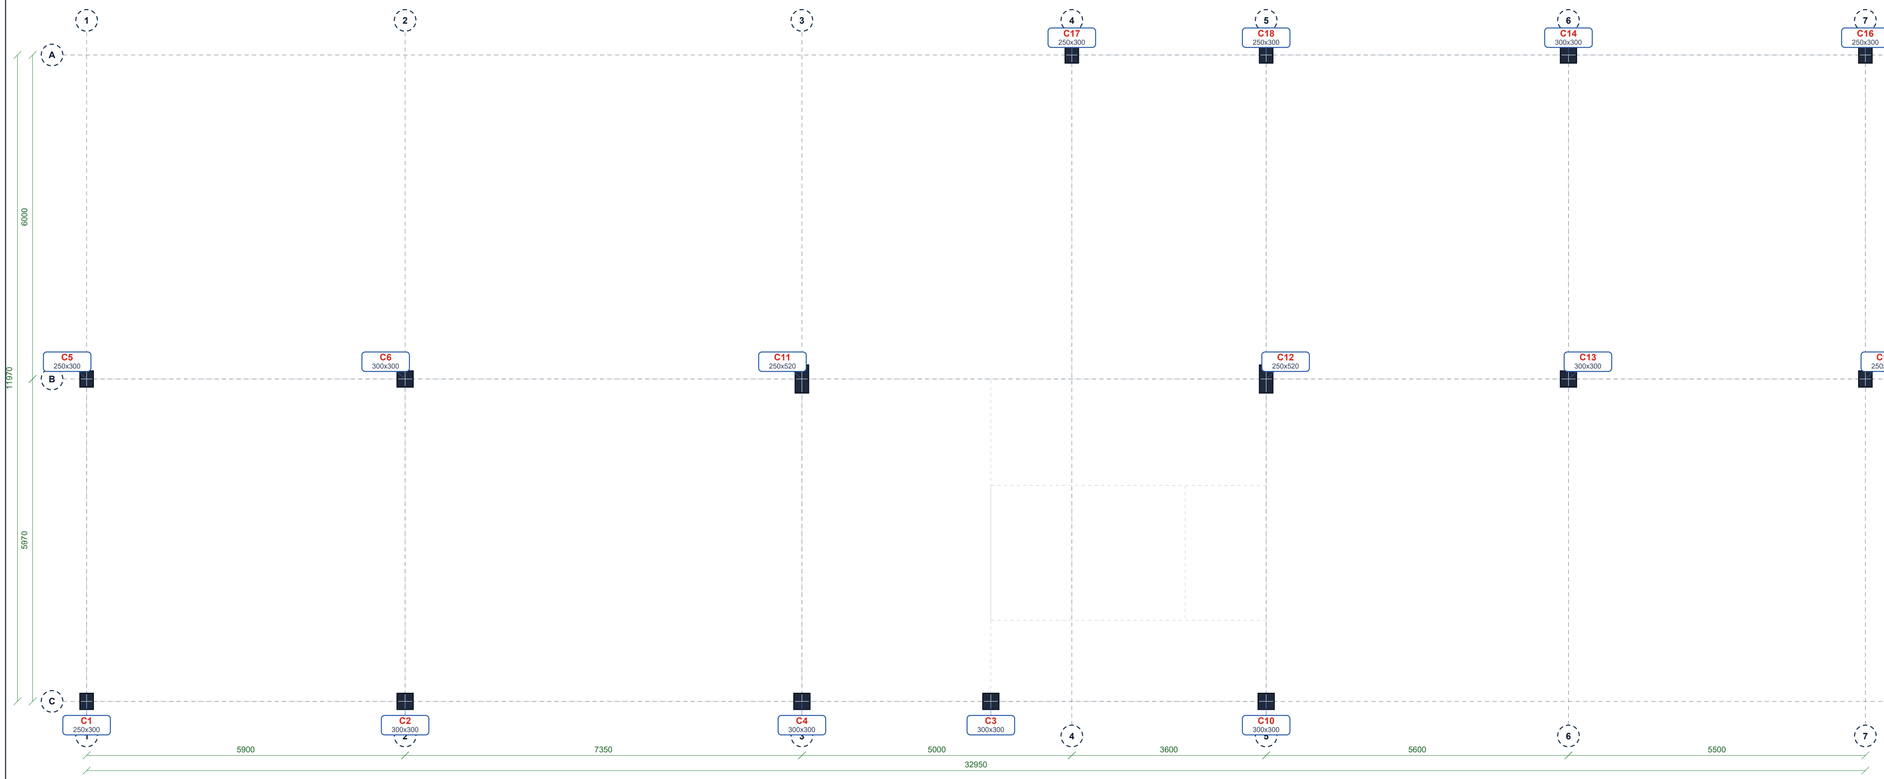

BẢNG THỐNG KÊ ĐỊNH VỊ CỘT (C1 → C18)

Mã Cột	Vị Trí Trục	Tiết Diện	Cốt Thép	Tầng
C1	(1-C)	250x300	4Φ18	T1-T3
C2	(2-C)	300x300	4Φ20	T1-T4
C3	(4*-C)	300x300	4Φ20	T1-T4
C4	(3-C)	300x300	4Φ20	T1-T4
C5	(1-B)	250x300	4Φ18	T1-T3
C6	(2-B)	300x300	4Φ20	T1-T4
C10	(5-C)	300x300	4Φ20	T1-T4
C11	(3-B)	250x520	8Φ20	T1-T4
C12	(5-B)	250x520	8Φ20	T1-T4
C13	(6-B)	300x300	4Φ20	T1-T4
C14	(6-A)	300x300	4Φ20	T1-T4
C15	(7-B)	250x300	4Φ18	T1-T3
C16	(7-A)	250x300	4Φ18	T1-T3
C17	(4-A)	250x300	4Φ18	T1-T4
C18	(5-A)	250x300	4Φ18	T1-T4

GHI CHÚ ĐỊNH VỊ VÀ BỐ TRÍ CỘT (TCVN 5574:2018):

1. Toàn bộ kích thước định vị ghi bằng milimét (mm), cao độ tính bằng mét (m). Tim cột trùng tim trục giao nhau.
2. Cột C11, C12 tiết diện 250x520 là cột cấy lớn chịu lực chính giảng giữa nhà trục B. Các cột C1, C5, C15, C16 dừng ở Tầng 3.
3. Bê tông cột B22.5 (M300). Thép chủ CB400-V, thép đai CB240-T. Lớp bê tông bảo vệ c = 25mm.

DỰ ÁN: CẢI TẠO PHƯƠNG ÁN B

HẠNG MỤC: KẾT CẤU BÊ TÔNG CỐT THÉP (TCVN 5574:2018)

BẢN VẼ: MẶT BẰNG ĐỊNH VỊ & BỐ TRÍ CỘT

KÝ HIỆU: KC-COT-01 • TỶ LỆ: 1:100 • NGÀY: 2026-10-19