

BẢN VẼ CHI TIẾT ĐÀ KIỀNG DỌC THEO TRỤC A, B, C (TẦNG 1 / MÓNG)

DỰ ÁN: CẢI TẠO PHƯƠNG ÁN B • TCVN 5574:2018 • BỐ TRÍ THÉP XÉT ĐẾN TÁC ĐỘNG CỦA PHẢN LỰC ĐẤT NỀN ĐẨY LÊN


ĐÀ KIỀNG TRỤC A (DK-A) • L = 14.70m • 3 NHỊP (TCVN 5574:2018 - ĐÀ KIỀNG CHỊU PHẢN LỰC ĐẤT)

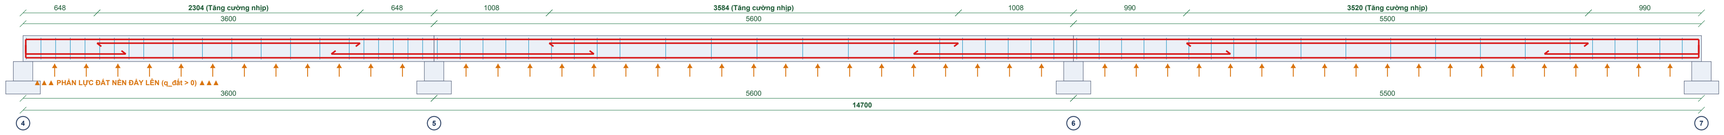


MẶT CẮT 1-1 (GIỮA NHỊP A)
[CĂNG THỚ TRÊN DO PHẢN LỰC ĐẤT]

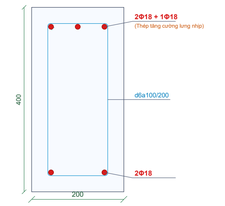


MẶT CẮT 2-2 (GỐI CỘT A)
[CĂNG THỚ DƯỚI DO CỘT TỰA ĐÈ XUỐNG]

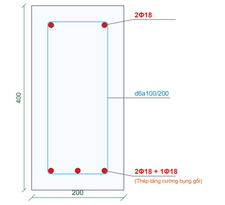


ĐÀ KIỀNG TRỤC B (DK-B) • L = 32.95m • 5 NHỊP (TCVN 5574:2018 - ĐÀ KIỀNG CHỊU PHẢN LỰC ĐẤT)

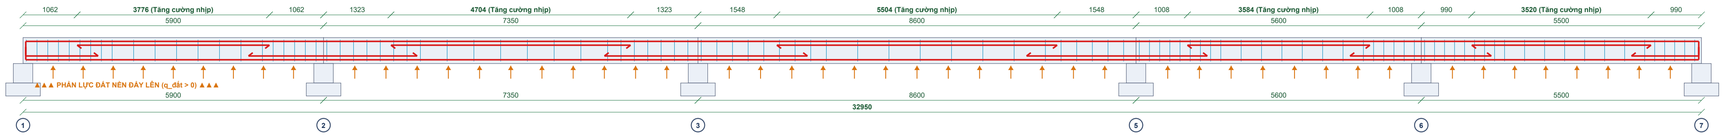


MẶT CẮT 1-1 (GIỮA NHỊP B)
[CĂNG THỚ TRÊN DO PHẢN LỰC ĐẤT]

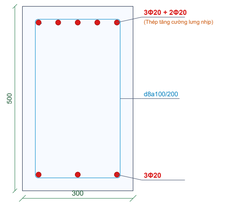


MẶT CẮT 2-2 (GỐI CỘT B)
[CĂNG THỚ DƯỚI DO CỘT TỰA ĐÈ XUỐNG]

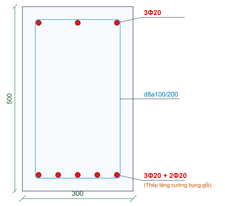


ĐÀ KIỀNG TRỤC C (DK-C) • L = 21.85m • 4 NHỊP (TCVN 5574:2018 - ĐÀ KIỀNG CHỊU PHẢN LỰC ĐẤT)

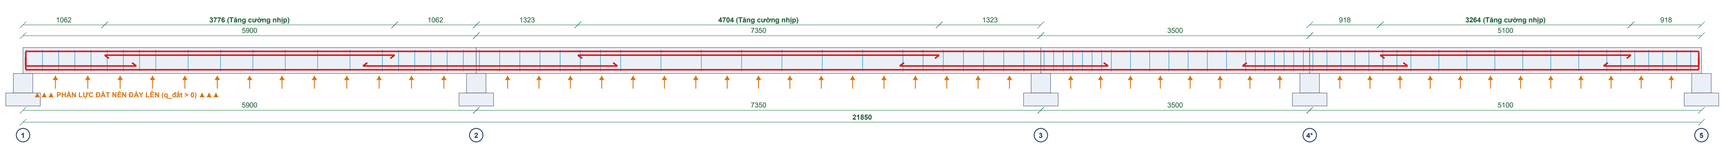

MẶT CẮT 1-1 (GIỮA NHỊP C)
[CĂNG THỚ TRÊN DO PHẢN LỰC ĐẤT]

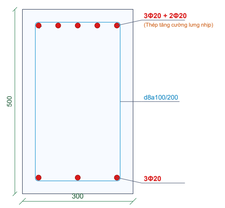

MẶT CẮT 2-2 (GỐI CỘT C)
[CĂNG THỚ DƯỚI DO CỘT TỰA ĐÈ XUỐNG]

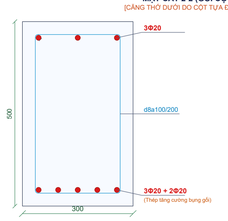

GHI CHÚ NGUYÊN LÝ BỐ TRÍ THÉP ĐÀ KIỀNG CHỊU PHẢN LỰC ĐẤT NỀN ĐẨY LÊN:

- NGUYÊN LÝ PHẢN LỰC ĐẨY TỪ ĐẤT LÊN (q_đất): Đà kiềng tựa trên nền đất chịu áp lực phản lực đất tác dụng từ dưới lên.
- Do phản lực đẩy từ dưới lên, mô-men uốn tại GIỮA NHỊP gây căng thớ TRÊN (Lưng dầm), tại VỊ TRÍ GỐI (chân cột/đài móng) gây căng thớ DƯỚI (Bụng dầm).
- Cốt thép tăng cường NHỊP bố trí ở LỚP TRÊN (LƯNG DẦM), chiều dài cắt thép 0.65L. Cốt thép tăng cường GỐI bố trí ở LỚP DƯỚI (BỤNG DẦM), chiều dài neo 0.25L mỗi bên.
- Thép chủ trên và dưới chạy suốt liền tục đối xứng nhằm chống lún lệch, chống xoắn và tăng cường độ cứng giằng móng.
- Bê tông đà kiềng: Cấp độ bền B22.5 (M300), Thép chủ CB400-V, Thép đai CB240-T. Lớp bê tông bảo vệ c = 35mm (có bê tông lót móng dày 100mm).

DỰ ÁN: CẢI TẠO PHƯƠNG ÁN B

HẠNG MỤC: KẾT CẤU MÓNG & ĐÀ KIỀNG TRỤC A, B, C

BẢN VẼ: CHI TIẾT ĐÀ KIỀNG

KÝ HIỆU: KC-DK-01 • TỶ LỆ 1/50 - 1/25

NGÀY XUẤT: 2026-10-19

KHỔ GIẤY: A1 LANDSCAPE